REV	DESCRIPTION	DATE
A	FIRST ISSUE	2026-10-01

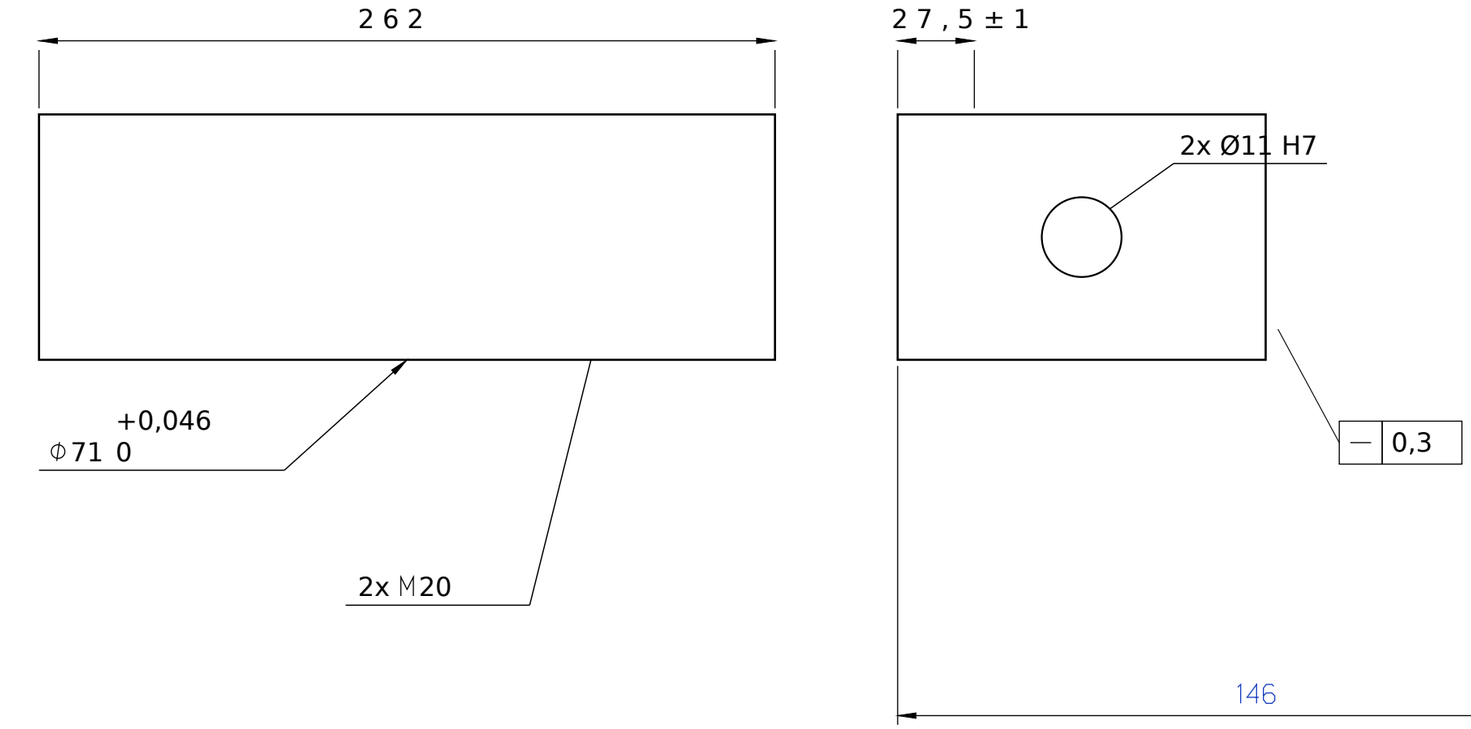

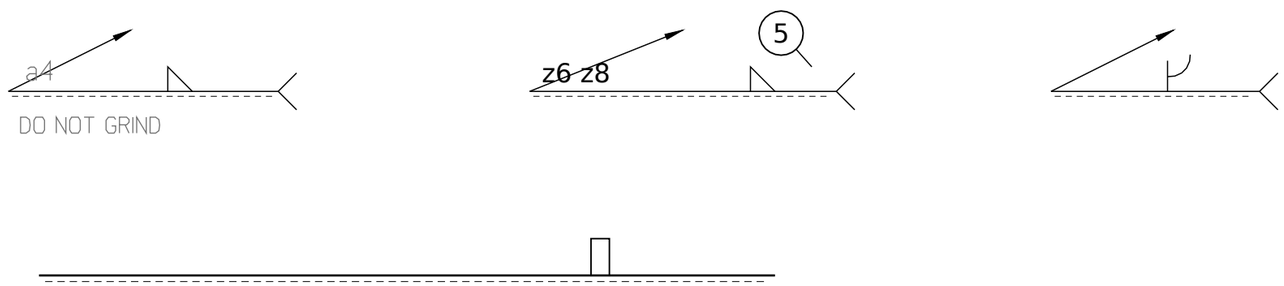

NOTES

1. WELDED CONSTRUCTION TOLERANCES ISO 13920-BF
2. REMOVE ALL BURRS

GENERAL TOLERANCE ±0.5

FICTITIOUS SAMPLE DRAWING

TITLE	WELD BRACKET	DWG NO.	WB-500
SCALE	1:2	MATERIAL	S355
DATE	2026-10-20	UNIT	mm
SHEET	1/1	REV	A