| REV | DESCRIPTION | DATE |
|---|---|---|
| A | FIRST ISSUE | 2026-10-01 |

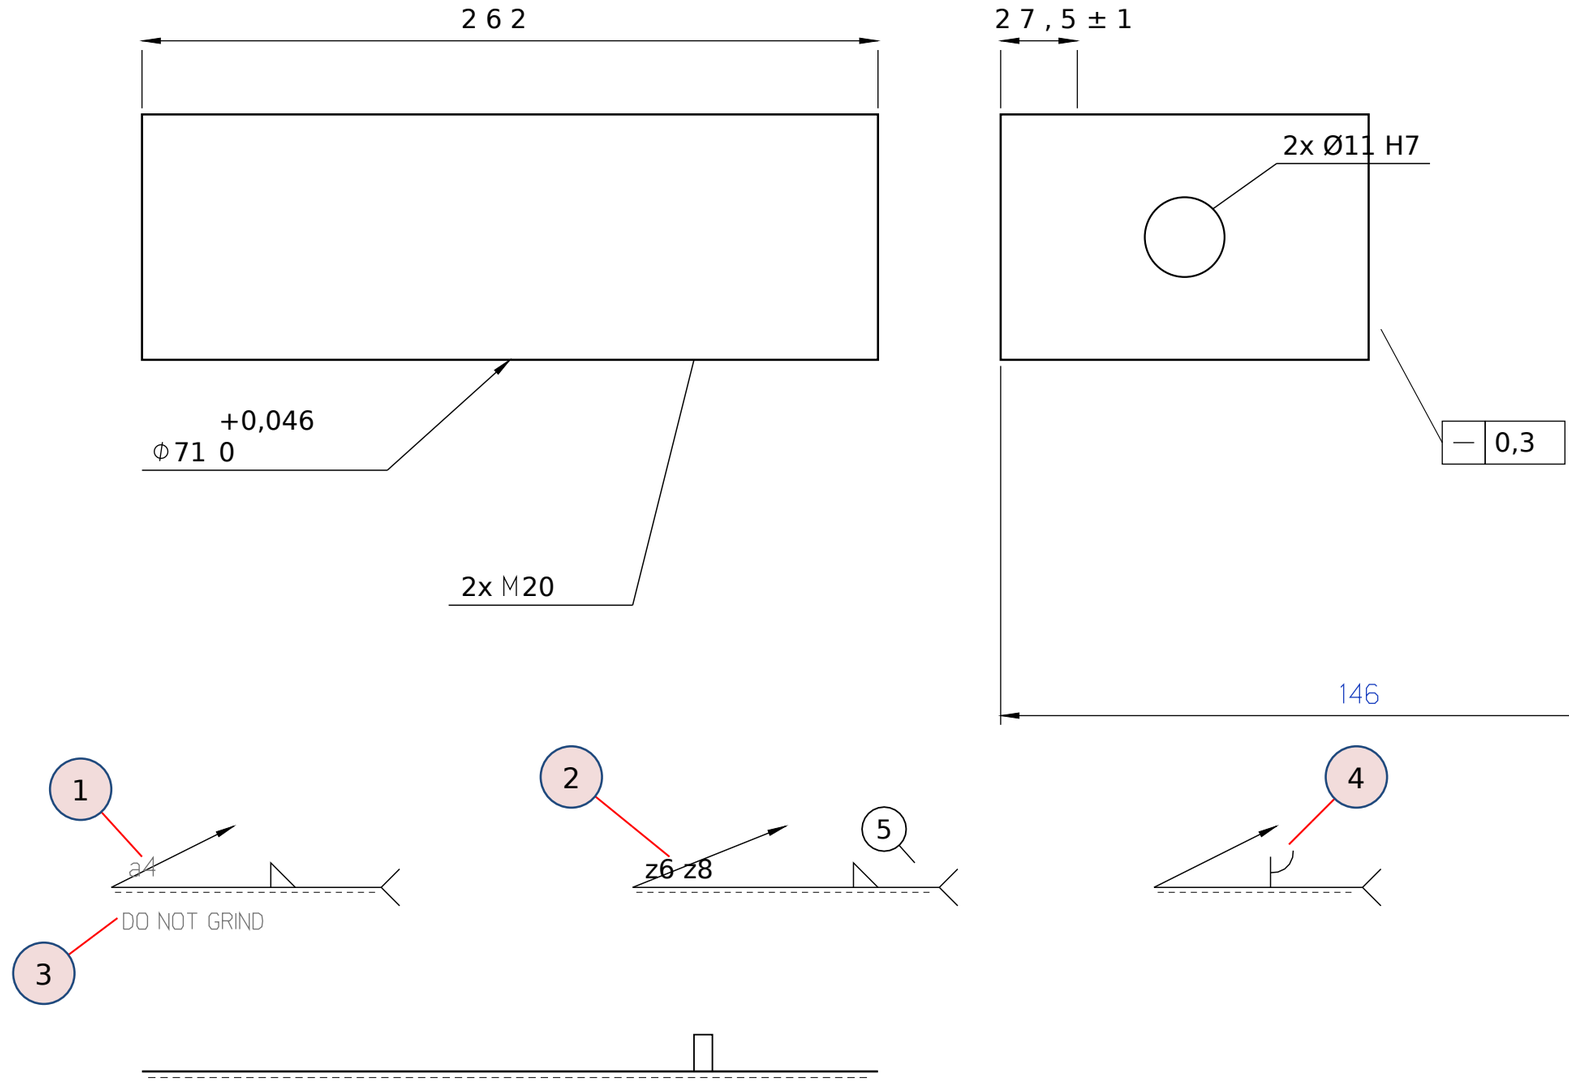


NOTES

1. WELDED CONSTRUCTION TOLERANCES ISO 13920-BF
2. REMOVE ALL BURRS

GENERAL TOLERANCE ±0.5

FICTITIOUS SAMPLE DRAWING

| | | | |
|---|---|---|---|
| TITLE | WELD BRACKET | DWG NO. | WB-500 |
| SCALE | 1:2 | MATERIAL | S355 |
| DATE | 2026-10-20 | UNIT | mm |
| SHEET | 1/1 | REV | A |